ПВЗ Ozon · заявка 544512

Тульская обл., Заокский р-н, Шеверняево, Северная ул., 30

Планировка и расстановка мебели по Руководству по брендингу Ozon (v.36 от 09.09.2026)

1. Помещение (по эскизу)

- Площадь без тамбура ≈ 59,7 м² (зал 43,7 + карман 2,74×5,3 = 14,5 + выступ ≈ 1,5) → формат L (от 40 м²).
- Тамбур 5,40×2,10 в площадь не входит. Вход с улицы через тамбур, дверь ПВЗ открывается наружу.
- Склад ≈ 20,0 м² (норма L: от 20), клиентская зона ≈ 38,6 м² (норма: от 20; ширина от 3 м).
- Склад отделяется новой перегородкой (на планах оранжевая).

2. Мебель (комплект S/M, 2 примерочные) — по списку из заказа

- Стойка ресепшен 0,9×0,6×1,0 м + приставной модуль 0,5×0,6 м
- Примерочные — ровно 2, двойной блок 2×(1,22×1,2×2,1 м), штора blackout, освещение внутри
- Стол проверки с выкатным контейнером 1,0×0,6 м (+ розетка 220 В рядом)
- Скамейка для примерки обуви 0,78×0,38 м, зеркало 0,8×1,6 м
- Стеллажи 1000×400×2000 мм (метал, 5 полок), 4 из них — отдельные для товаров продавцов
- Стены: RAL 7047 (светло-серый) или белый, матовые; потолок над примерочными — не глянцевый.

3. Проверка по правилам Ozon

- Вход → внешняя граница стойки: ≥ 1,5 м — выполнено (вар. А 4,4 м, вар. Б ≈ 3 м).
- Проходы в клиентской зоне ≥ 0,9 м; проходы на складе ≥ 1,0 м (1,94 м) — выполнено.
- Позади оператора 0,9–1,2 м; вход на склад рядом с оператором, ширина 0,95 м — выполнено.
- Подход к примерочным ≥ 0,9 м, мебель их не перекрывает; камеры не над примерочными.
- Камеры: минимум 2 — зал (виден стол проверки и оператор) и склад; стеллажи не закрывают обзор.
- Брендовая стена «Зебра» за стойкой, плакаты на высоте 2200 мм, табличка над столом проверки.
- Стеллажей на плане 14–15, для L рекомендовано от 17 — можно добавить второй ряд или увеличить склад.

4. Два варианта расстановки


- Вариант А: стойка в левом углу, дверь на склад с запада; примерочные вдоль правой стены, склад — «карман».
- Вариант Б: стойка перед складом (где были тарные ящики), склад позади неё; примерочные у стены склада.

5. Что проверить на месте

- Эскиз нарисован не в масштабе — приняты подписанные размеры: 6,0 · 5,3 · 2,10 · 2,74 · 2,2 · 2,5 · 2,3 м.
- Глубина нижнего выступа справа (≈ 0,7 м), положение окон и двери — оценка по рисунку.
- Проём 2,10 м в левом нижнем углу зала нужно закрыть перегородкой.
- Подключение света брендинга к электросети — согласовать с арендодателем и администрацией.


Страницы: 2 — план помещения · 3 — вариант А · 4 — вариант Б

Заявка 544512 · Шеверняево, Северная ул., 30 — ПЛАН ПОМЕЩЕНИЯ по эскизу (красный контур)
Площадь ПВЗ без тамбура ≈ 59.7 м² (зал 43.7 + карман 14.5 + выступ 1.5)

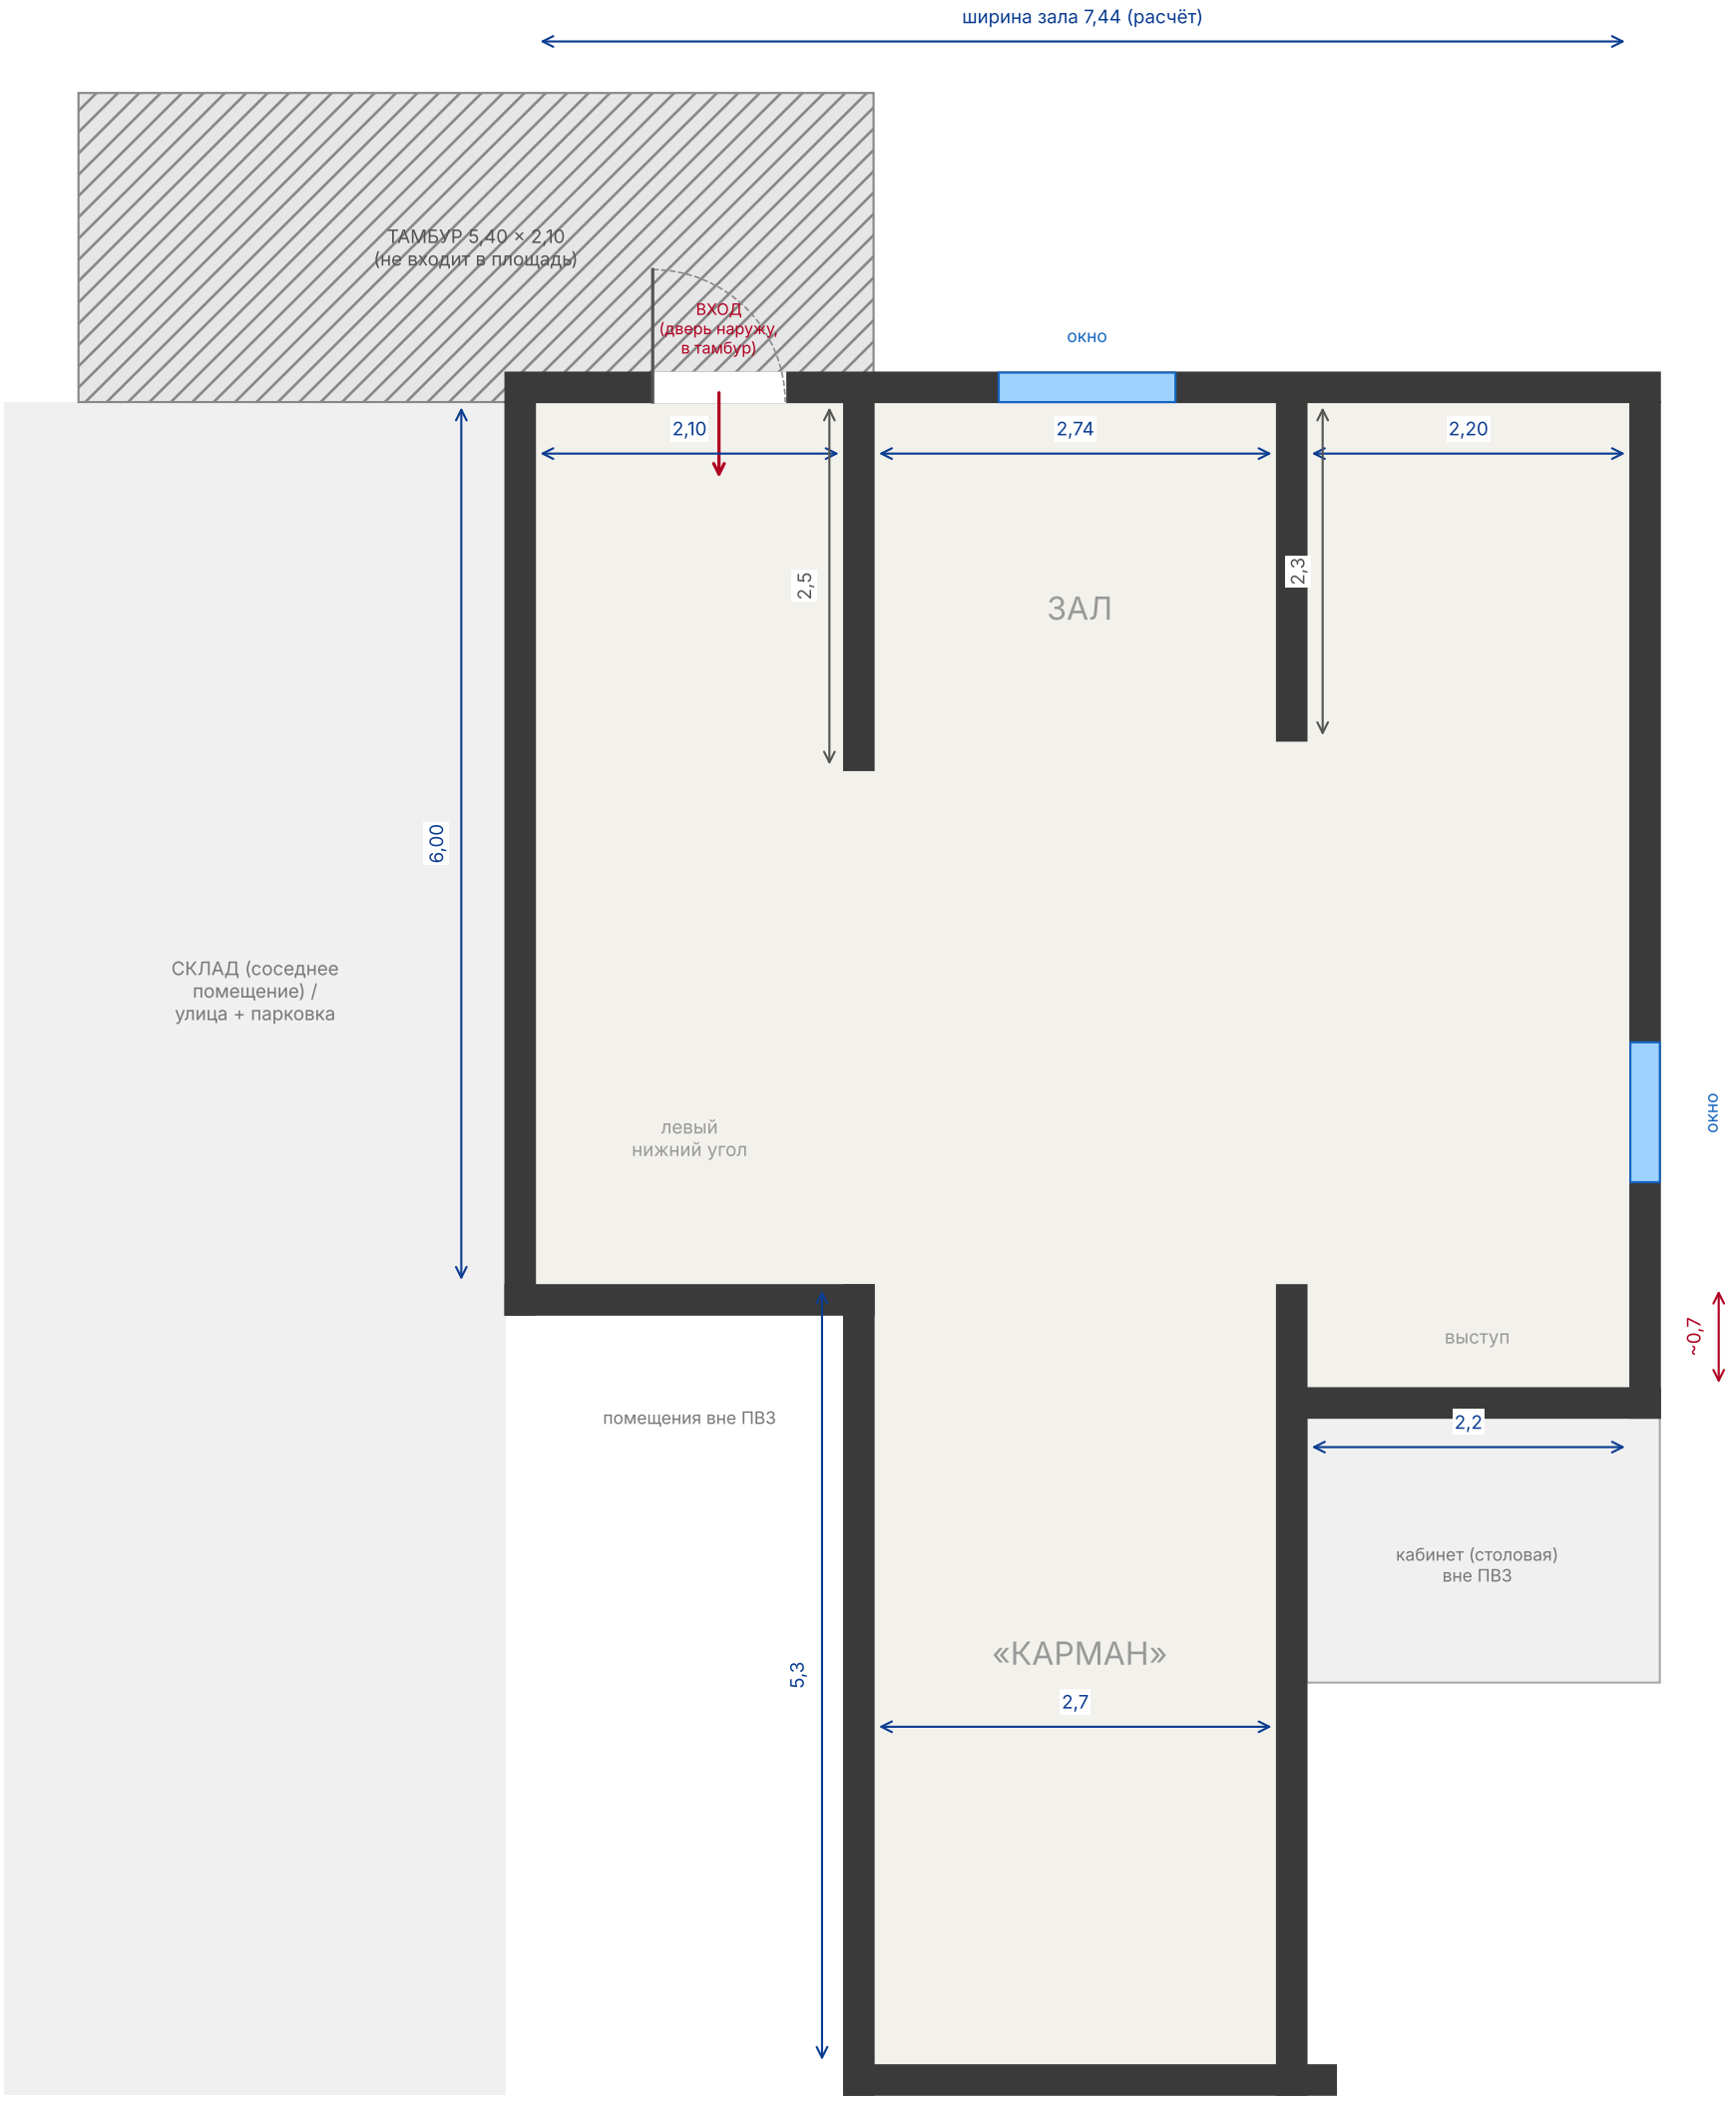


Эскиз нарисован не в масштабе: за основу взяты подписанные размеры. Проверьте рулеткой (особенно 6,0 · 5,3 · 0,7 м и положение окон).

Заявка 544512 · Шеверняево, Северная ул., 30 — РАССТАНОВКА МЕБЕЛИ (формат L, ≥ 40 м²)
Оранжевое — новые перегородки склада

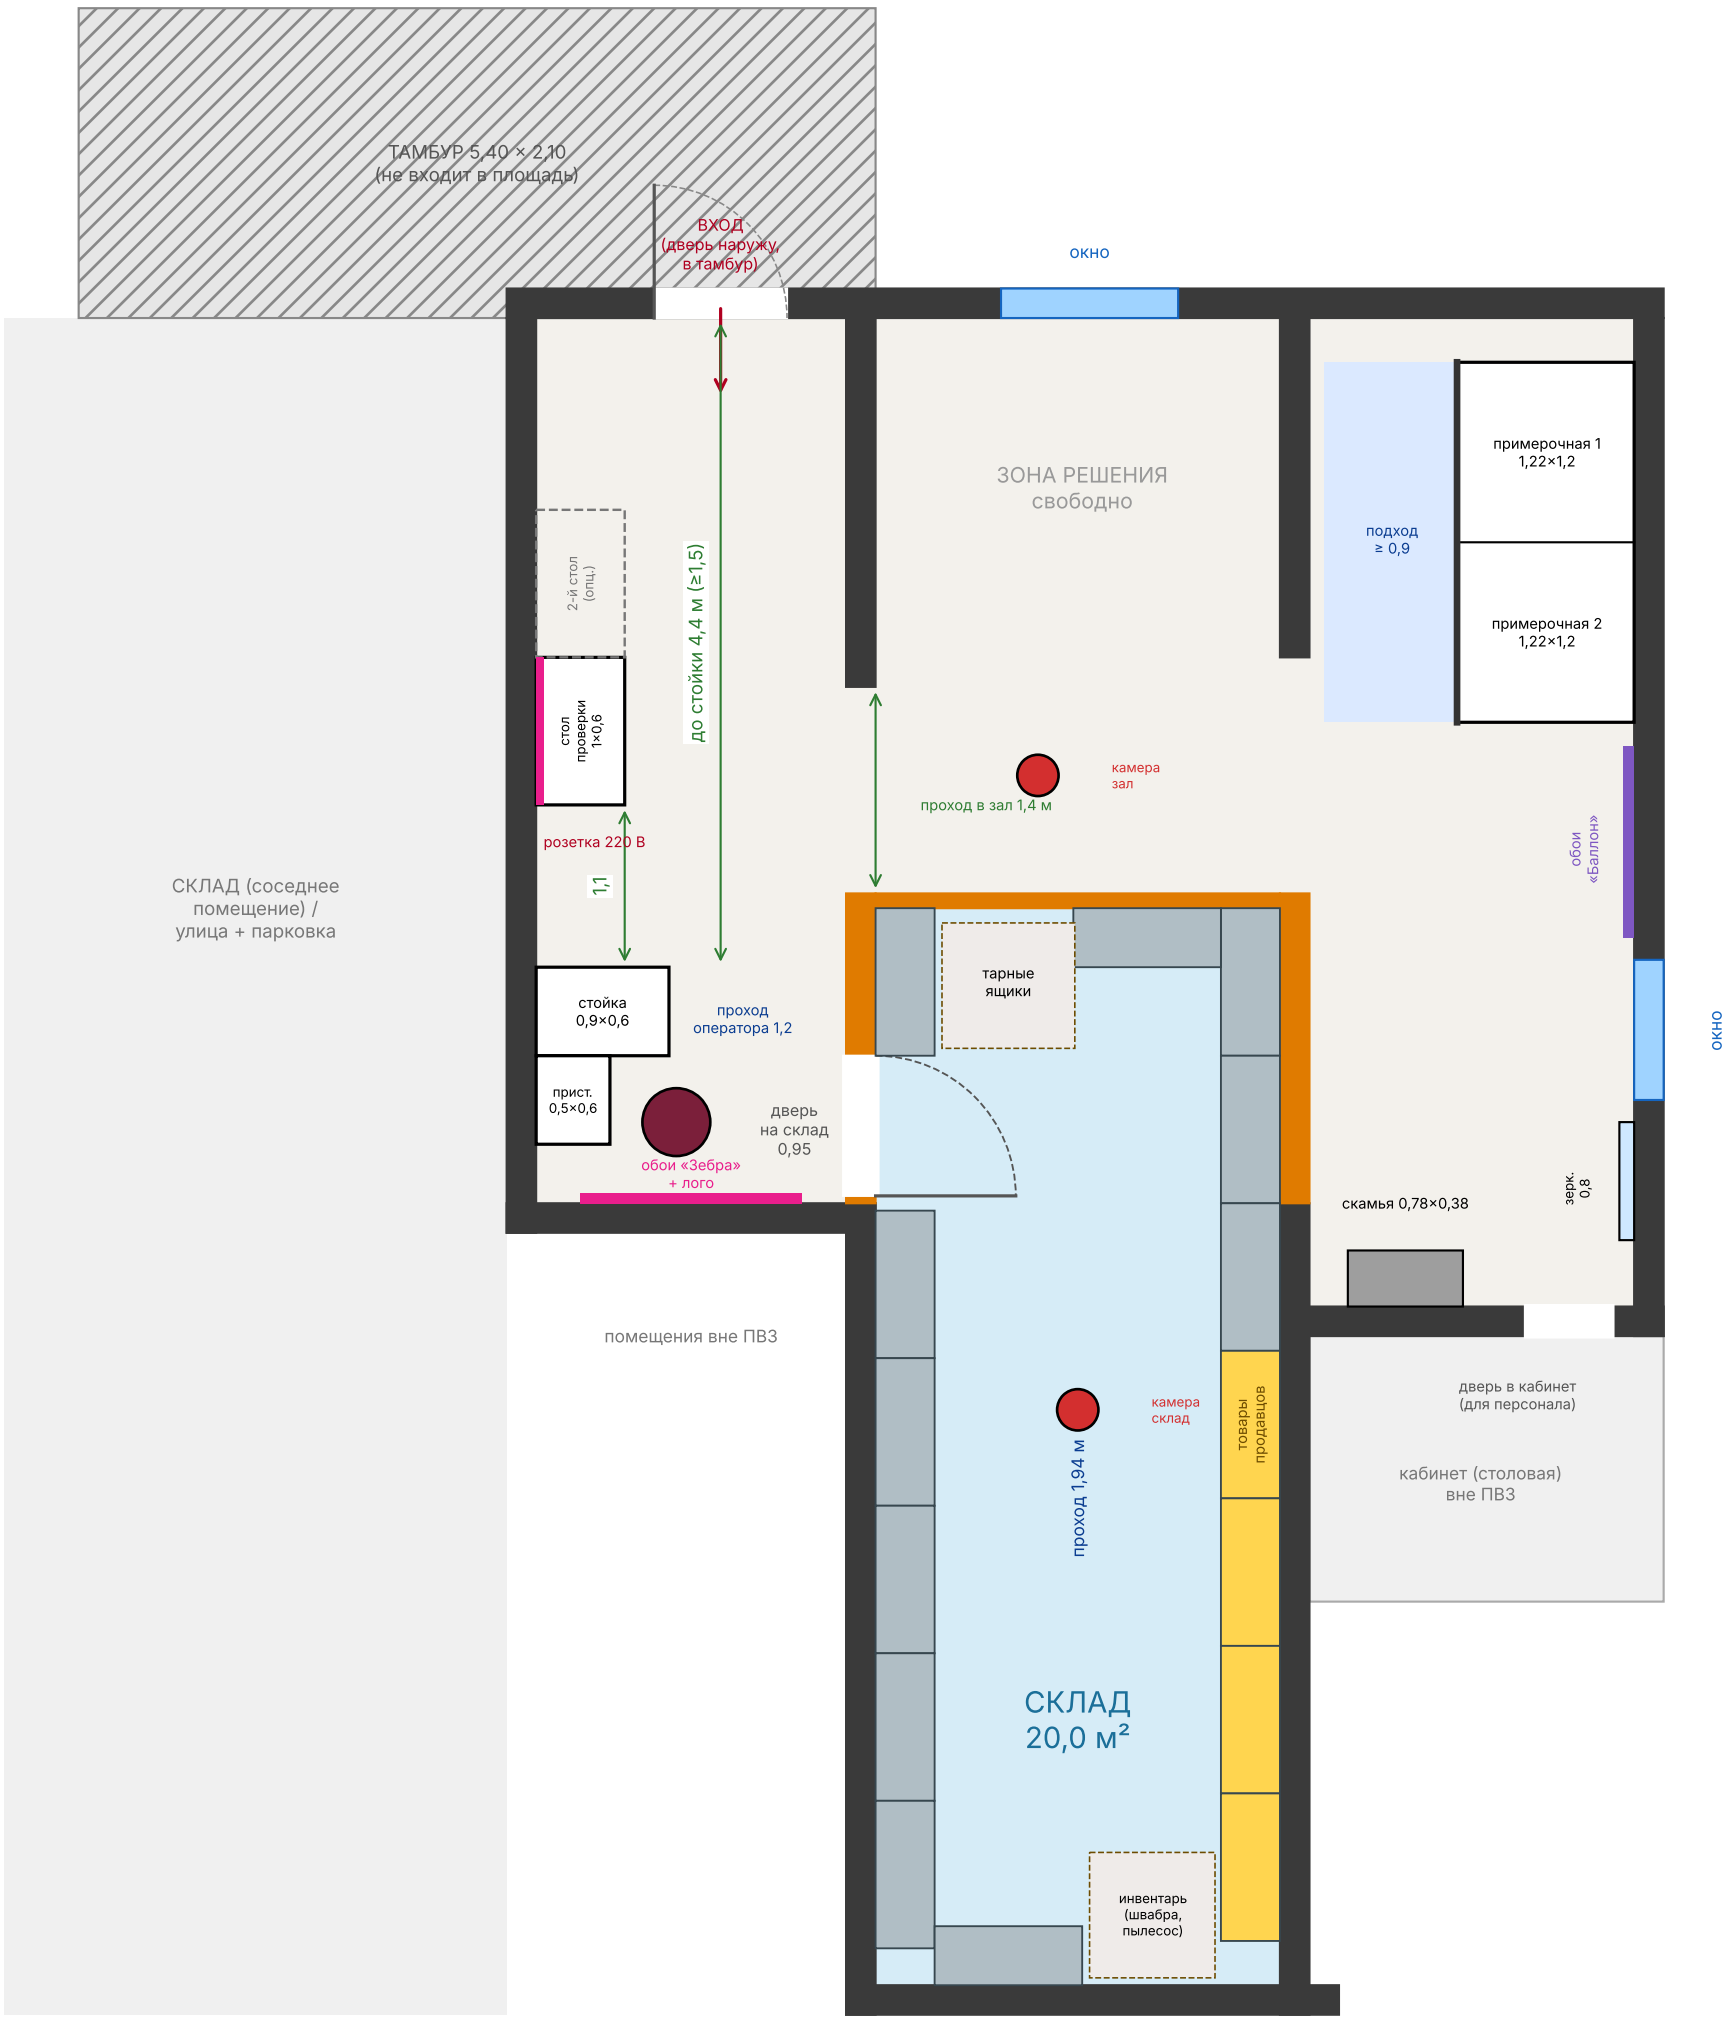

Всего ≈ 59.7 м² · склад ≈ 20,0 м² (норма L: ≥ 20) · клиентская зона ≈ 38.6 м² (≥ 20) · стеллажей 15 (рекомендовано для L: от 17) · примерочных 2 · проходы ≥ 0,9 м

Заявка 544512 · Шеверняево, Северная ул., 30 — РАССТАНОВКА, ВАРИАНТ Б
Стойка перед складом (вместо тарных ящиков), склад позади, примерочные у стены склада

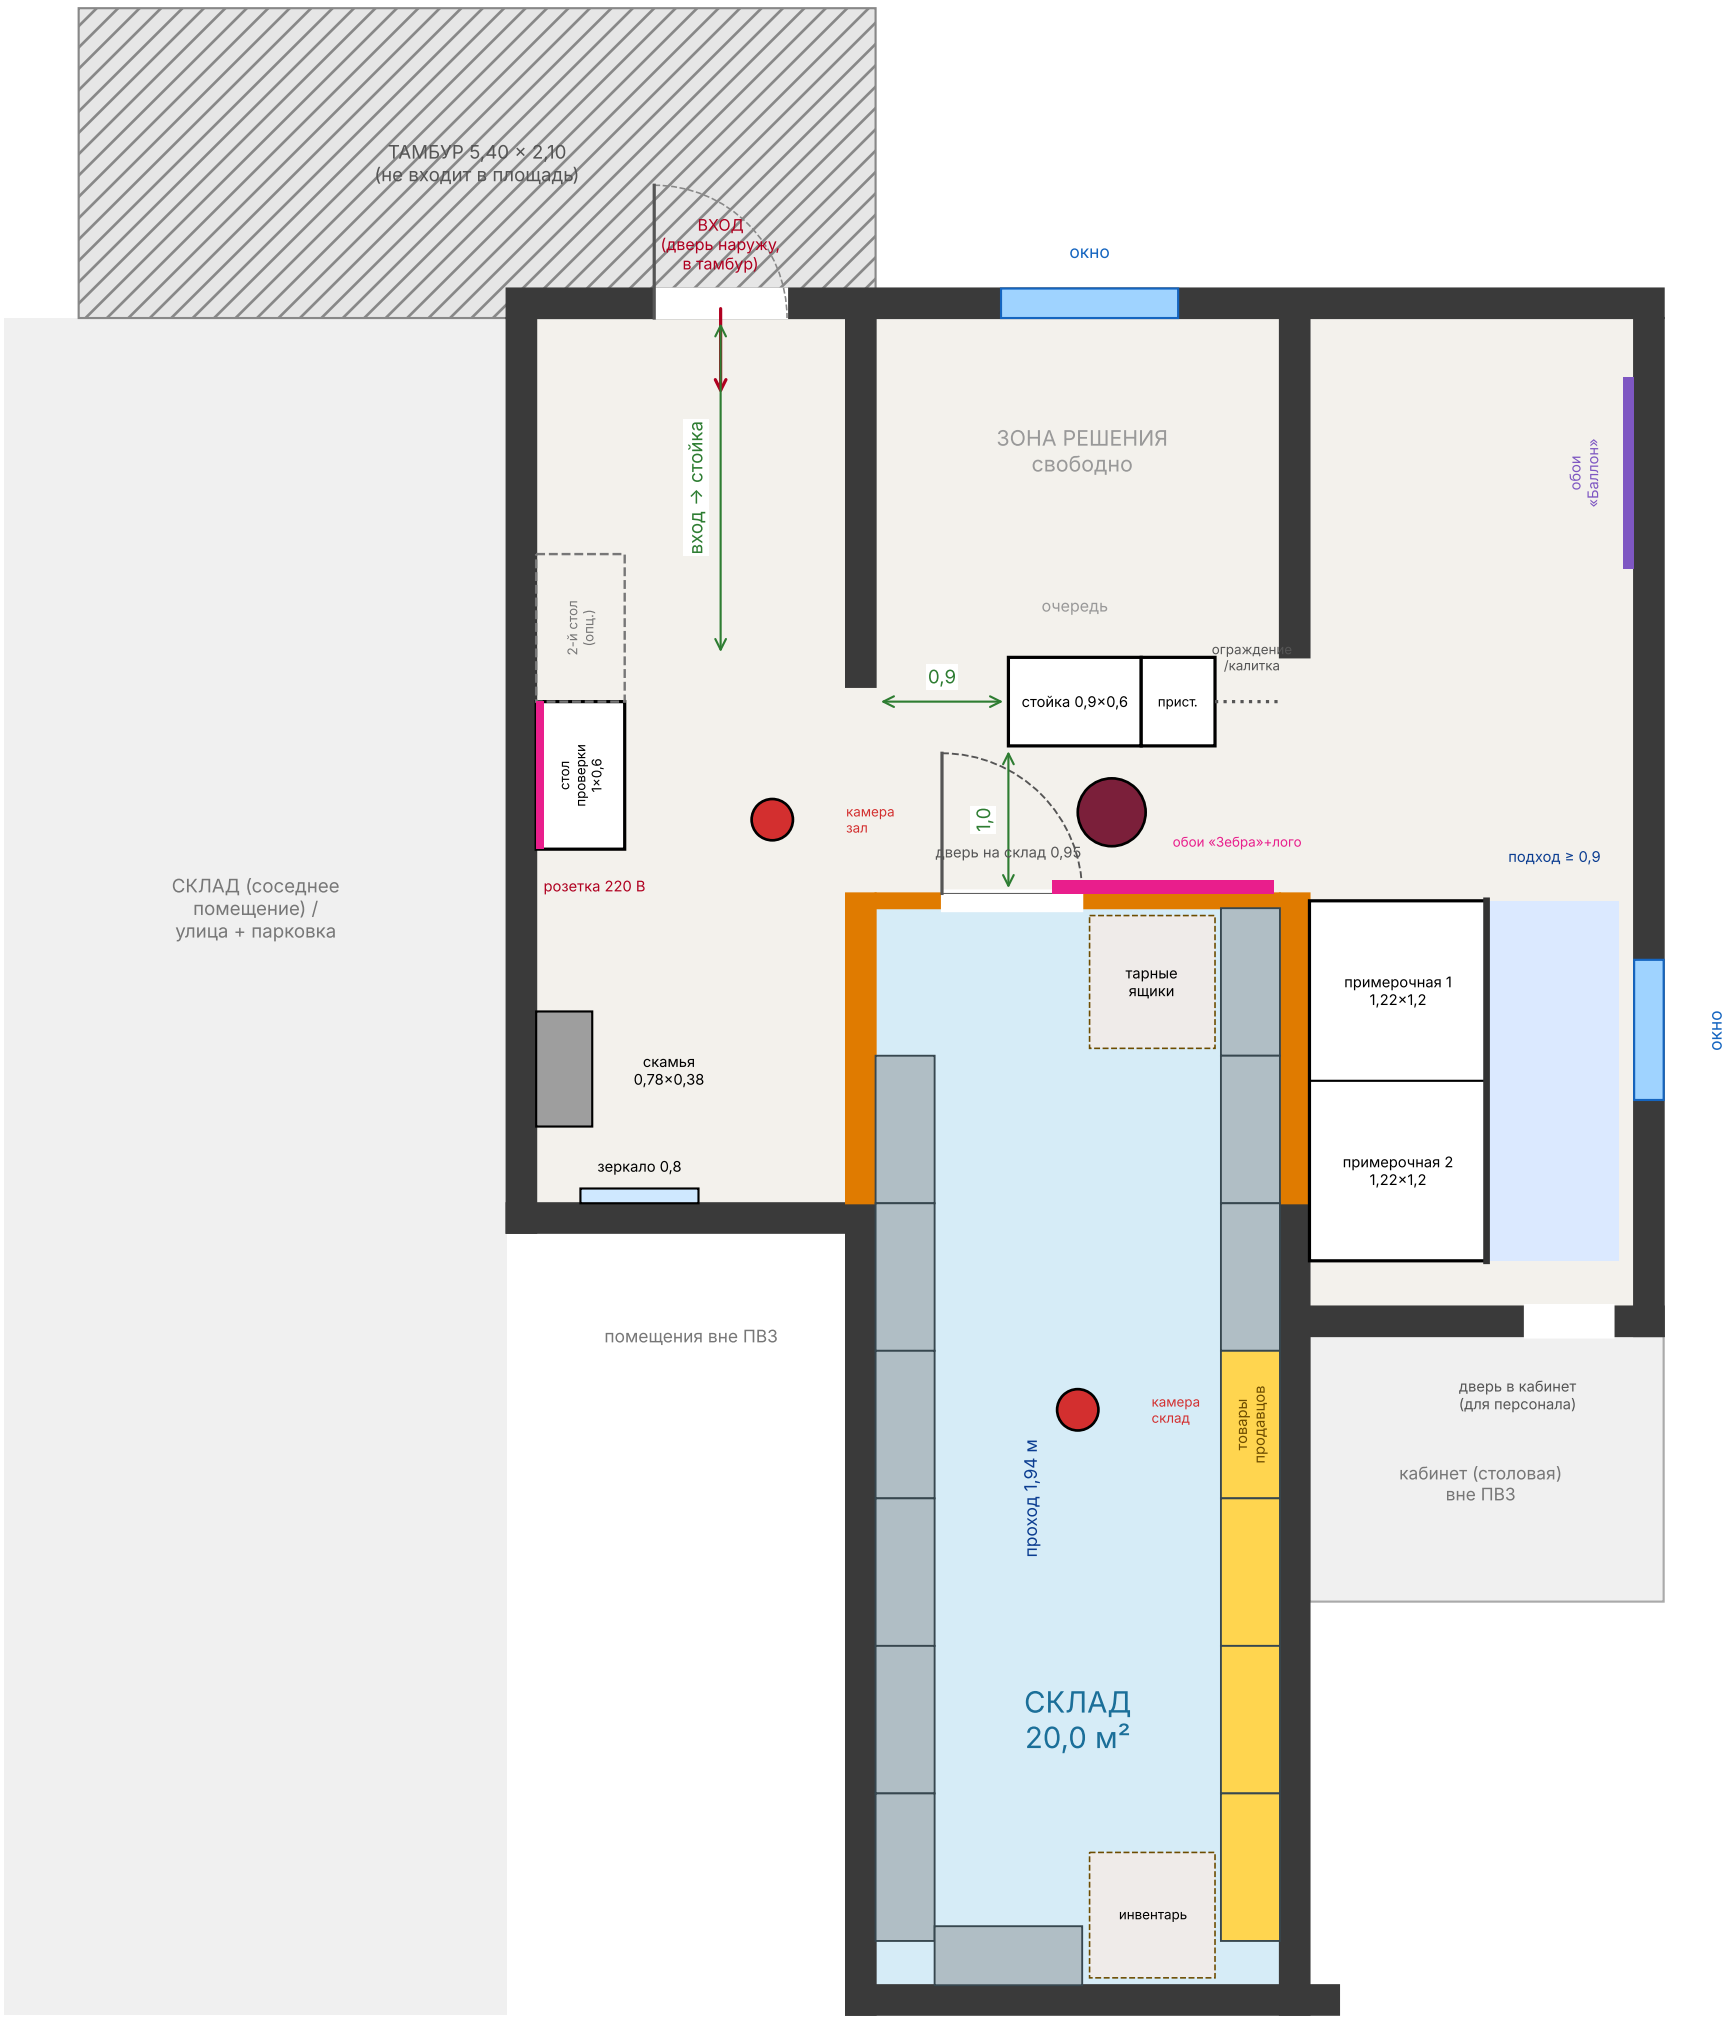

Всего ≈ 59.7 м² · склад ≈ 20,0 м² · клиентская зона ≈ 38.6 м² · стеллажей 14 (рекоменд. для L: от 17) · примерочных 2 · проходы ≥ 0,9 м