
Заявка 544512 · эскиз №2 — КАК НАРИСОВАНО (все надписи сохранены)
Геометрия по подписям; положение мебели — по рисунку (оценка). Тёмно-синие точки — «САМ» (камеры).

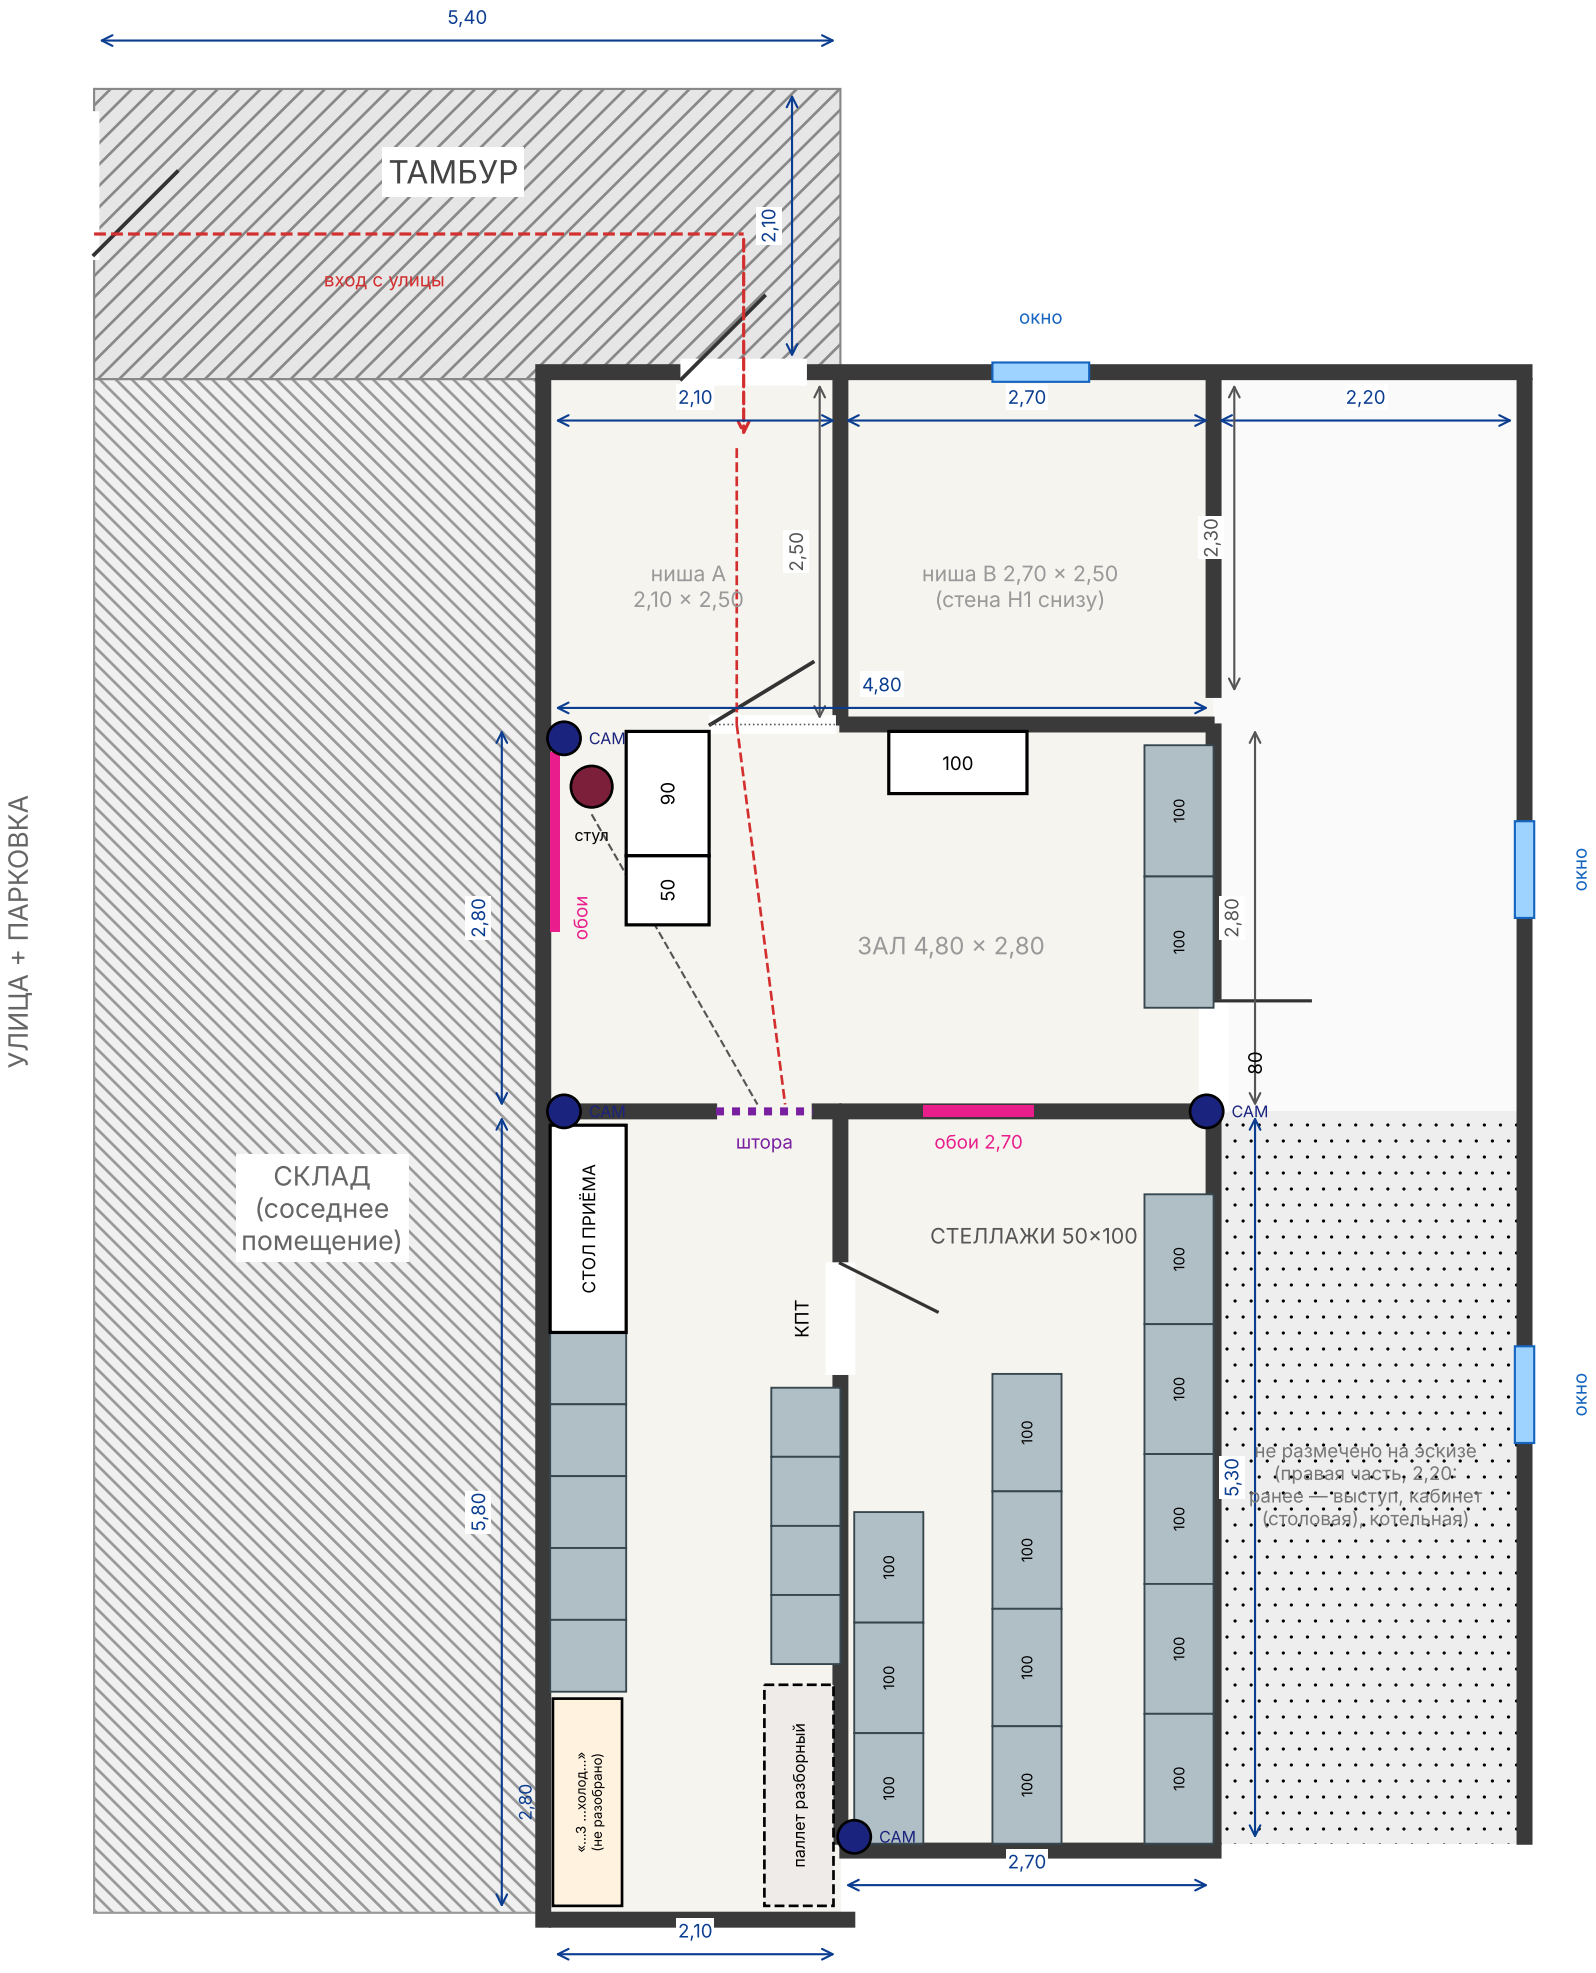


Не разобрано на эскизе: надпись у нижнего левого элемента («...3 ...холод...»), «КПТ» (так и оставил), «2,30» или «2,40» у правого простенка, что за «100» у стены Н1.

# Экспертная проверка эскиза №2 по Руководству Ozon (v.36)

Заявка 544512 · Шеверняево, Северная ул., 30

## Площади (по подписям)

• Зал 4,80×2,80 = 13,4 м² · ниша A 2,10×2,50 = 5,25 · ниша B 2,70×2,50 = 6,75

• Левая колонка 2,10×5,80 = 12,2 м² · карман 2,70×5,30 = 14,3 м² → склад-зона 26,5 м²

• Итого, если ПВЗ = зал + левая колонка + карман: 39,9 м²; + ниша A = 45,1; + ниша B = 51,9 м²

## Нарушения и риски (по убыванию важности)

1. НЕТ ПРИМЕРОЧНЫХ. Нужно минимум 2 (комплект 2×1,22×1,2 м). Единственное подходящее место — ниша B (2,70 м ≥ 2,44 м):

Ozon допускает «примерочные в нише». Для этого стену H1 над нишей B нужно убрать, окно изнутри закрыть блоком.

2. СТОЙКА У ВХОДА. От двери H1 до стойки ≈ 0 м, нужно ≥ 1,5 м; очередь упирается в дверь и в зону решения (≥ 0,8 м).

3. ПРОХОД ОПЕРАТОРА 0,7 м (между левой стеной и стойкой) — нужно ≥ 0,9 м; позади оператора 0,9–1,2 м не выдержано.

4. ВХОД НА СКЛАД ЧЕРЕЗ ШТОРУ ≈ 0,7 м — нужно ≥ 0,9 м; лучше дверь, рядом с оператором. Нужна дверь и в стене H2.

5. ПРОХОДЫ В КАРМАНЕ 0,57–0,65 м (стеллажи 0,5 м слева, «остров» и справа) — нужно ≥ 1,0 м. Остров убрать или сузить.

6. КЛИЕНТСКАЯ ЗОНА: зал 13,4 м² < 17 м² (для формата M) / 20 м² (L). С нишей B — 20,2 м² ✓; с нишей A — 25,4 м².

7. Глубина стеллажей 0,5 м: рекомендовано 1000/1200×400 мм. Стеллажи товаров продавцов — отдельно, в зоне камеры.

8. Стеллажи 2×(0,5×1,0) в клиентском зале у правой стены уменьшают просторную зону — лучше убрать на склад.

9. Стол «100» у стены H1: нужен проход ≥ 0,9 м со всех сторон и розетка 220 В; в эскизе проход слева 0,6 м.


## Что выполнено

✓ Камеры: 4 шт. (минимум 2: зал и склад); не над примерочными. ✓ Стол приёма и склад отделены от клиентской зоны.

✓ Бренд-обои на стене у входа в карман; дверь 0,8 м из зала; запас по складу (26,5 м² при норме 20 для L).

Следующая страница — рекомендуемая расстановка (вариант Г), исправляющая пп. 1–6 в тех же стенах.

Заявка 544512 · ВАРИАНТ Г — рекомендуемая расстановка (те же стены, замечания эксперта учтены)
Оранжевое — что нужно изменить в конструкции. Все проходы ≥ 0,9 м (клиентская зона) и ≥ 1,0 м (склад).

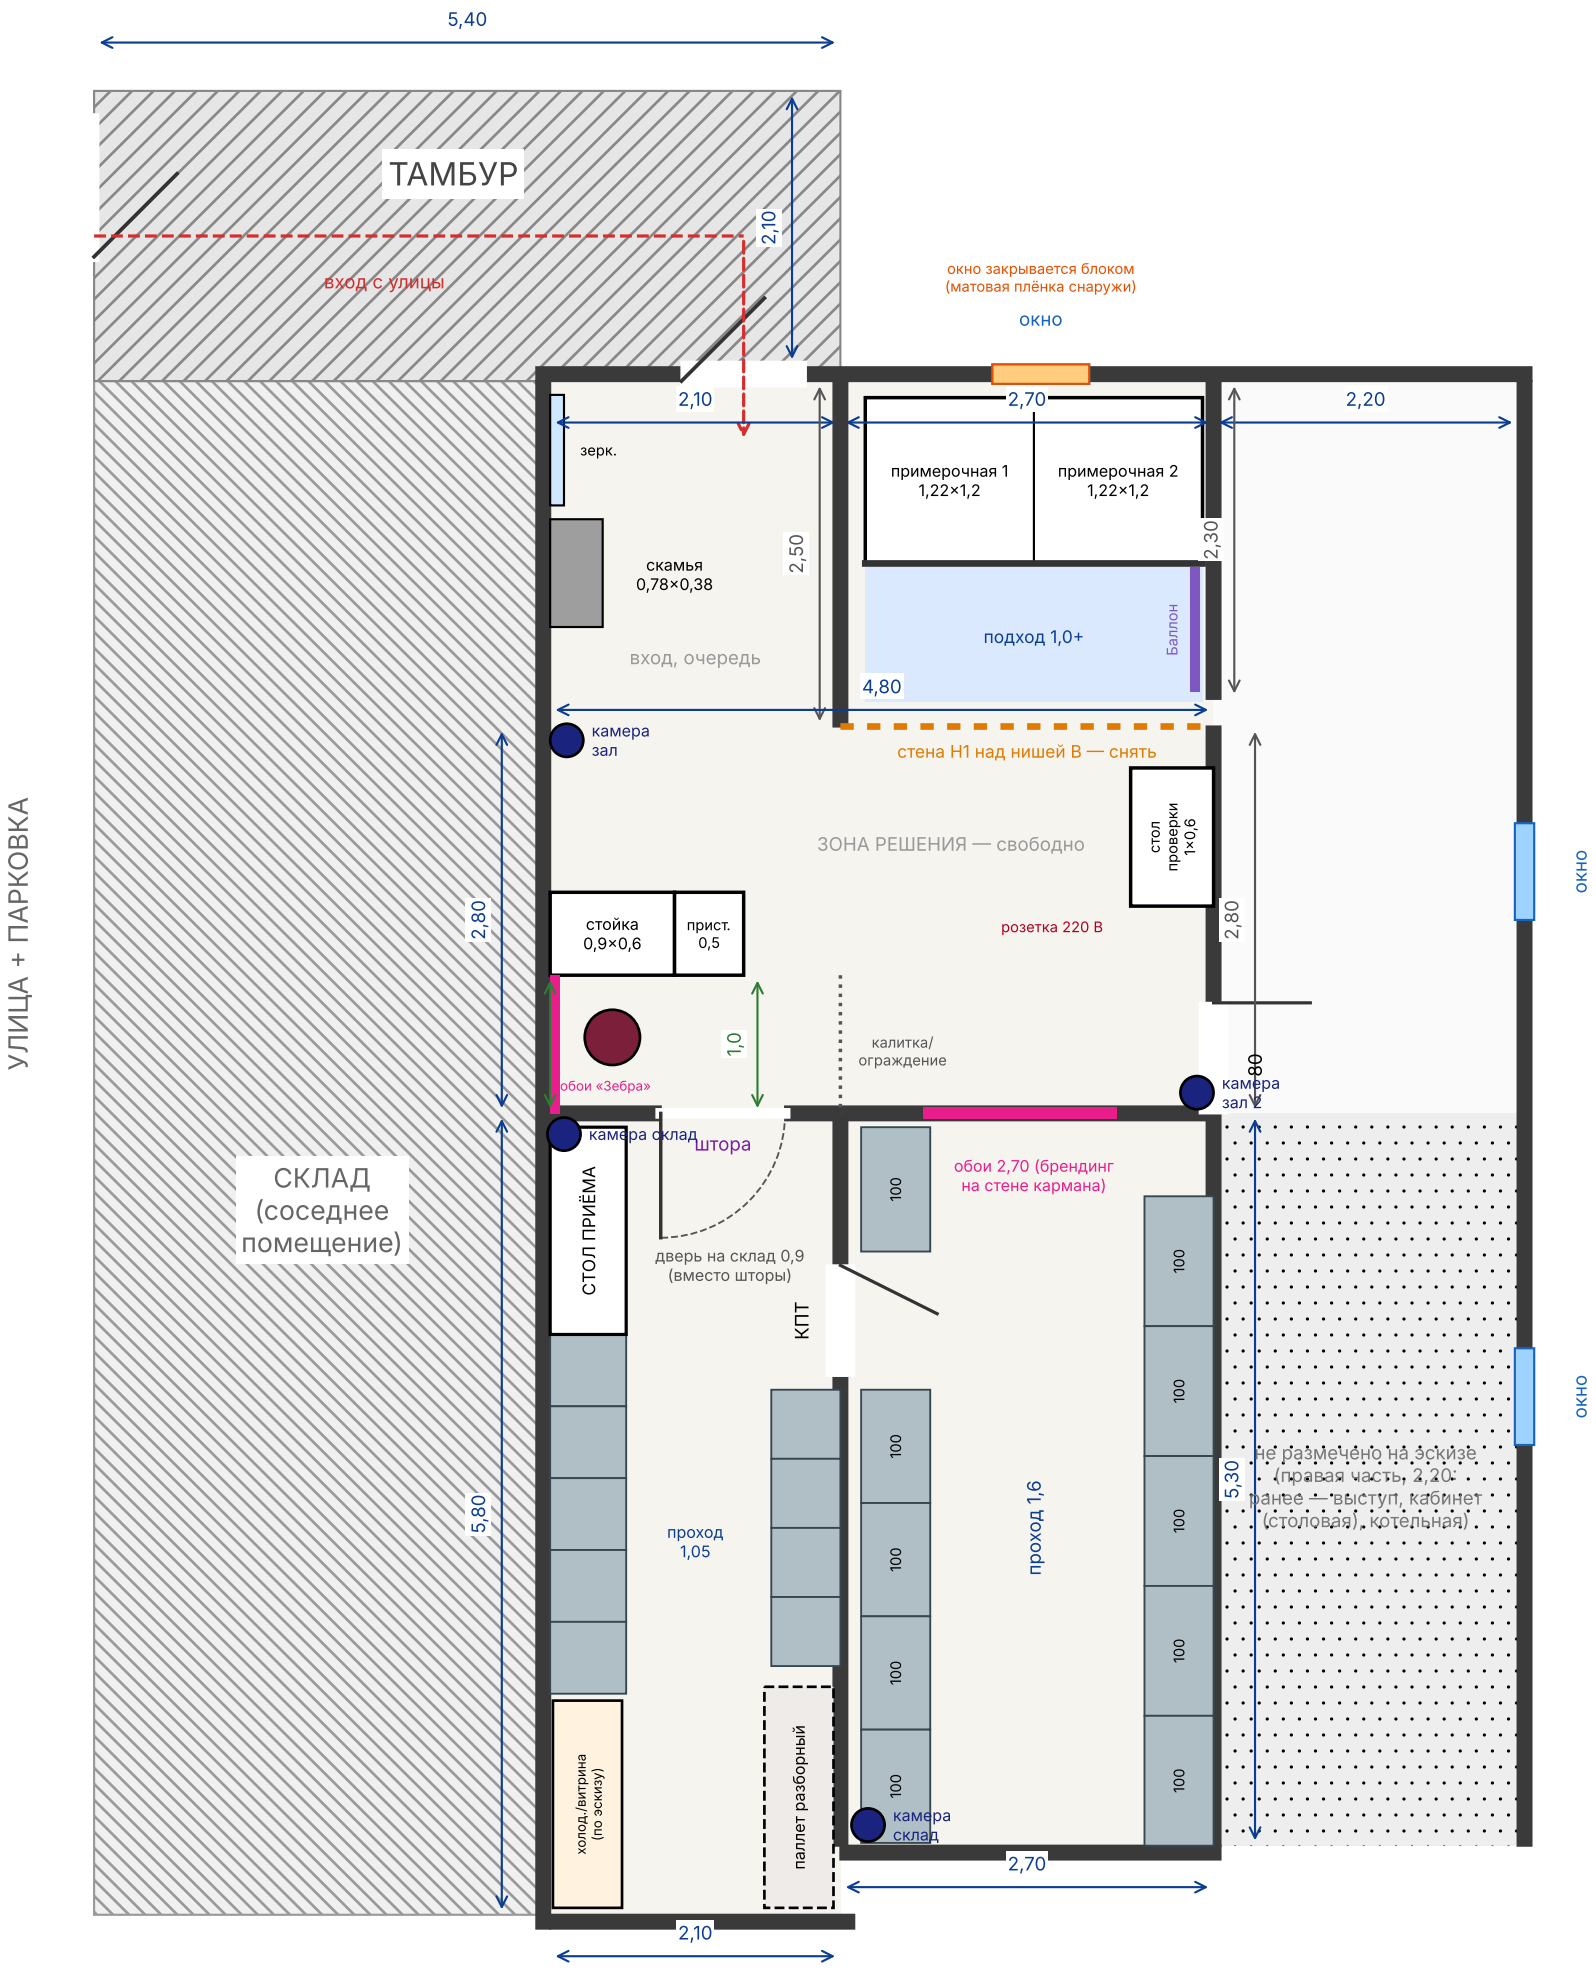


Клиентская зона: зал 13,4 + ниша В 6,75 = 20.2 м² (≥ 20 ✓) · склад-зона 26,5 м² (≥ 20 ✓) · примерочных 2 ✓ · вход→стойка 3,7 м ✓ · проход оператора 1,0 м ✓